




PLANTA BAIXA DRIVE-IN
Escala: 1:125

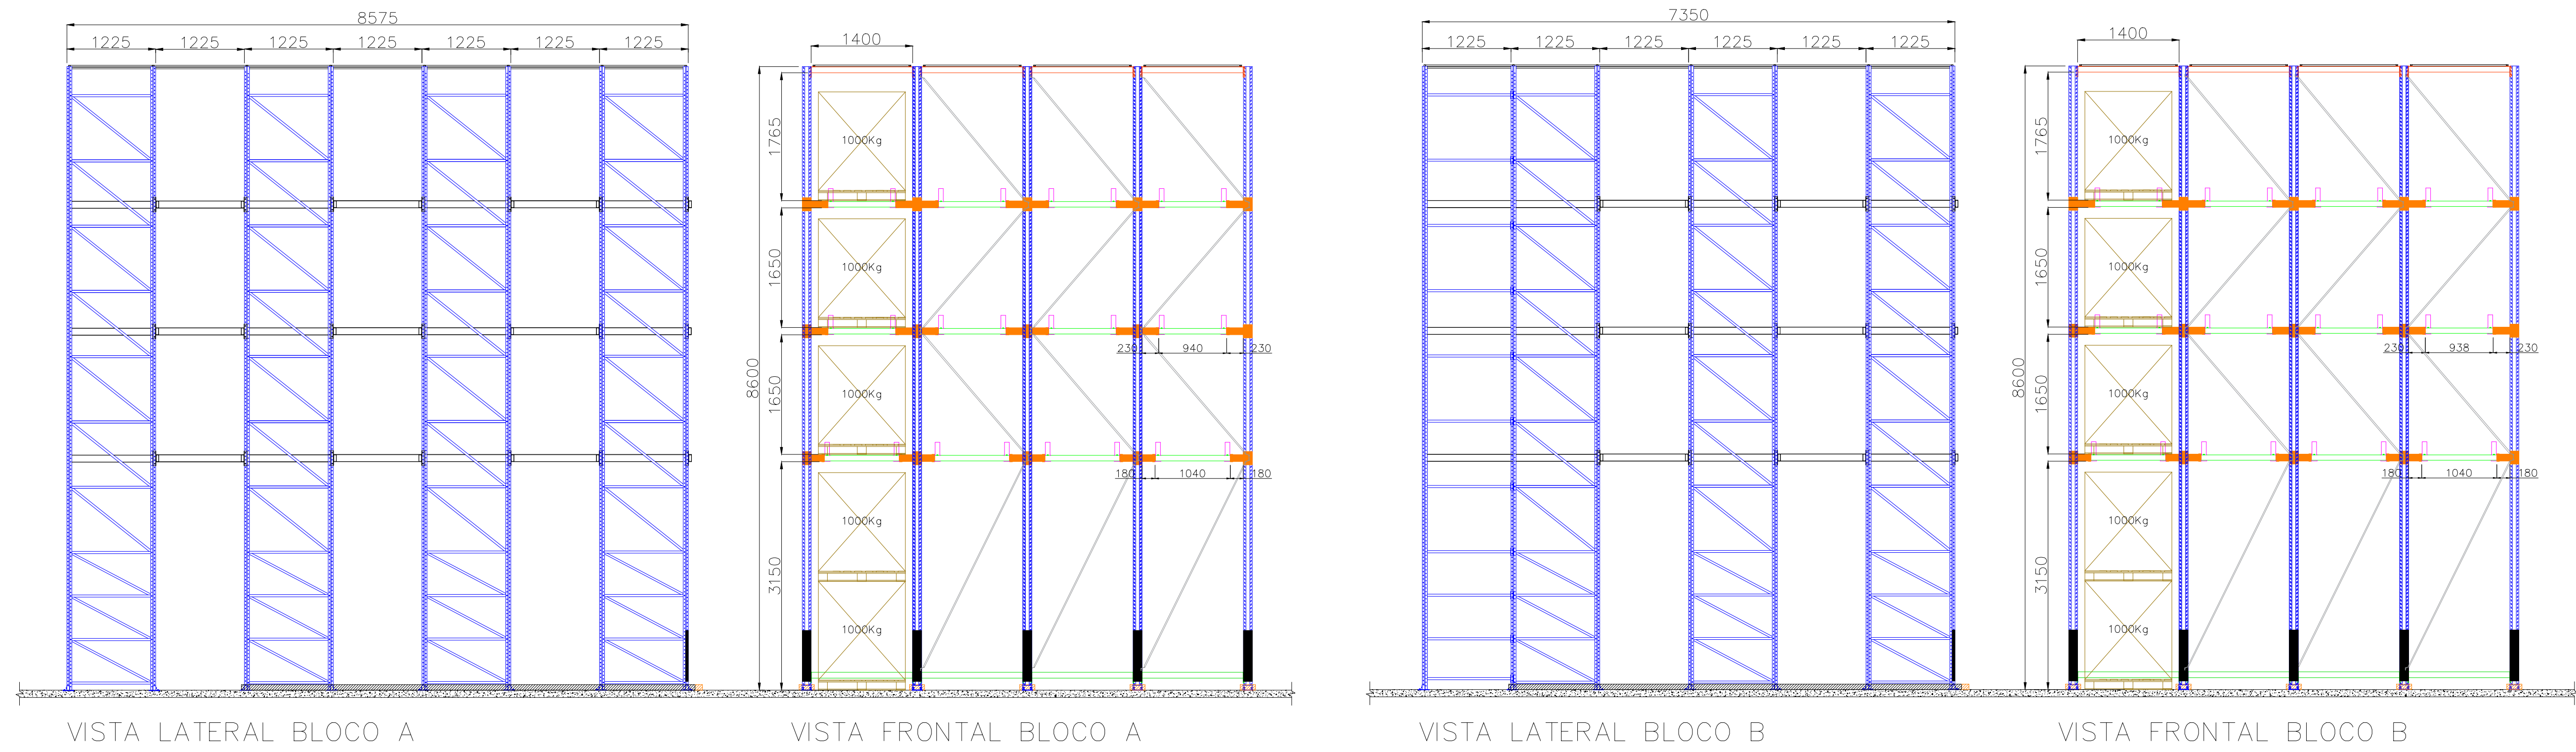

CORTES DRIVE-IN
Escala: 1:50

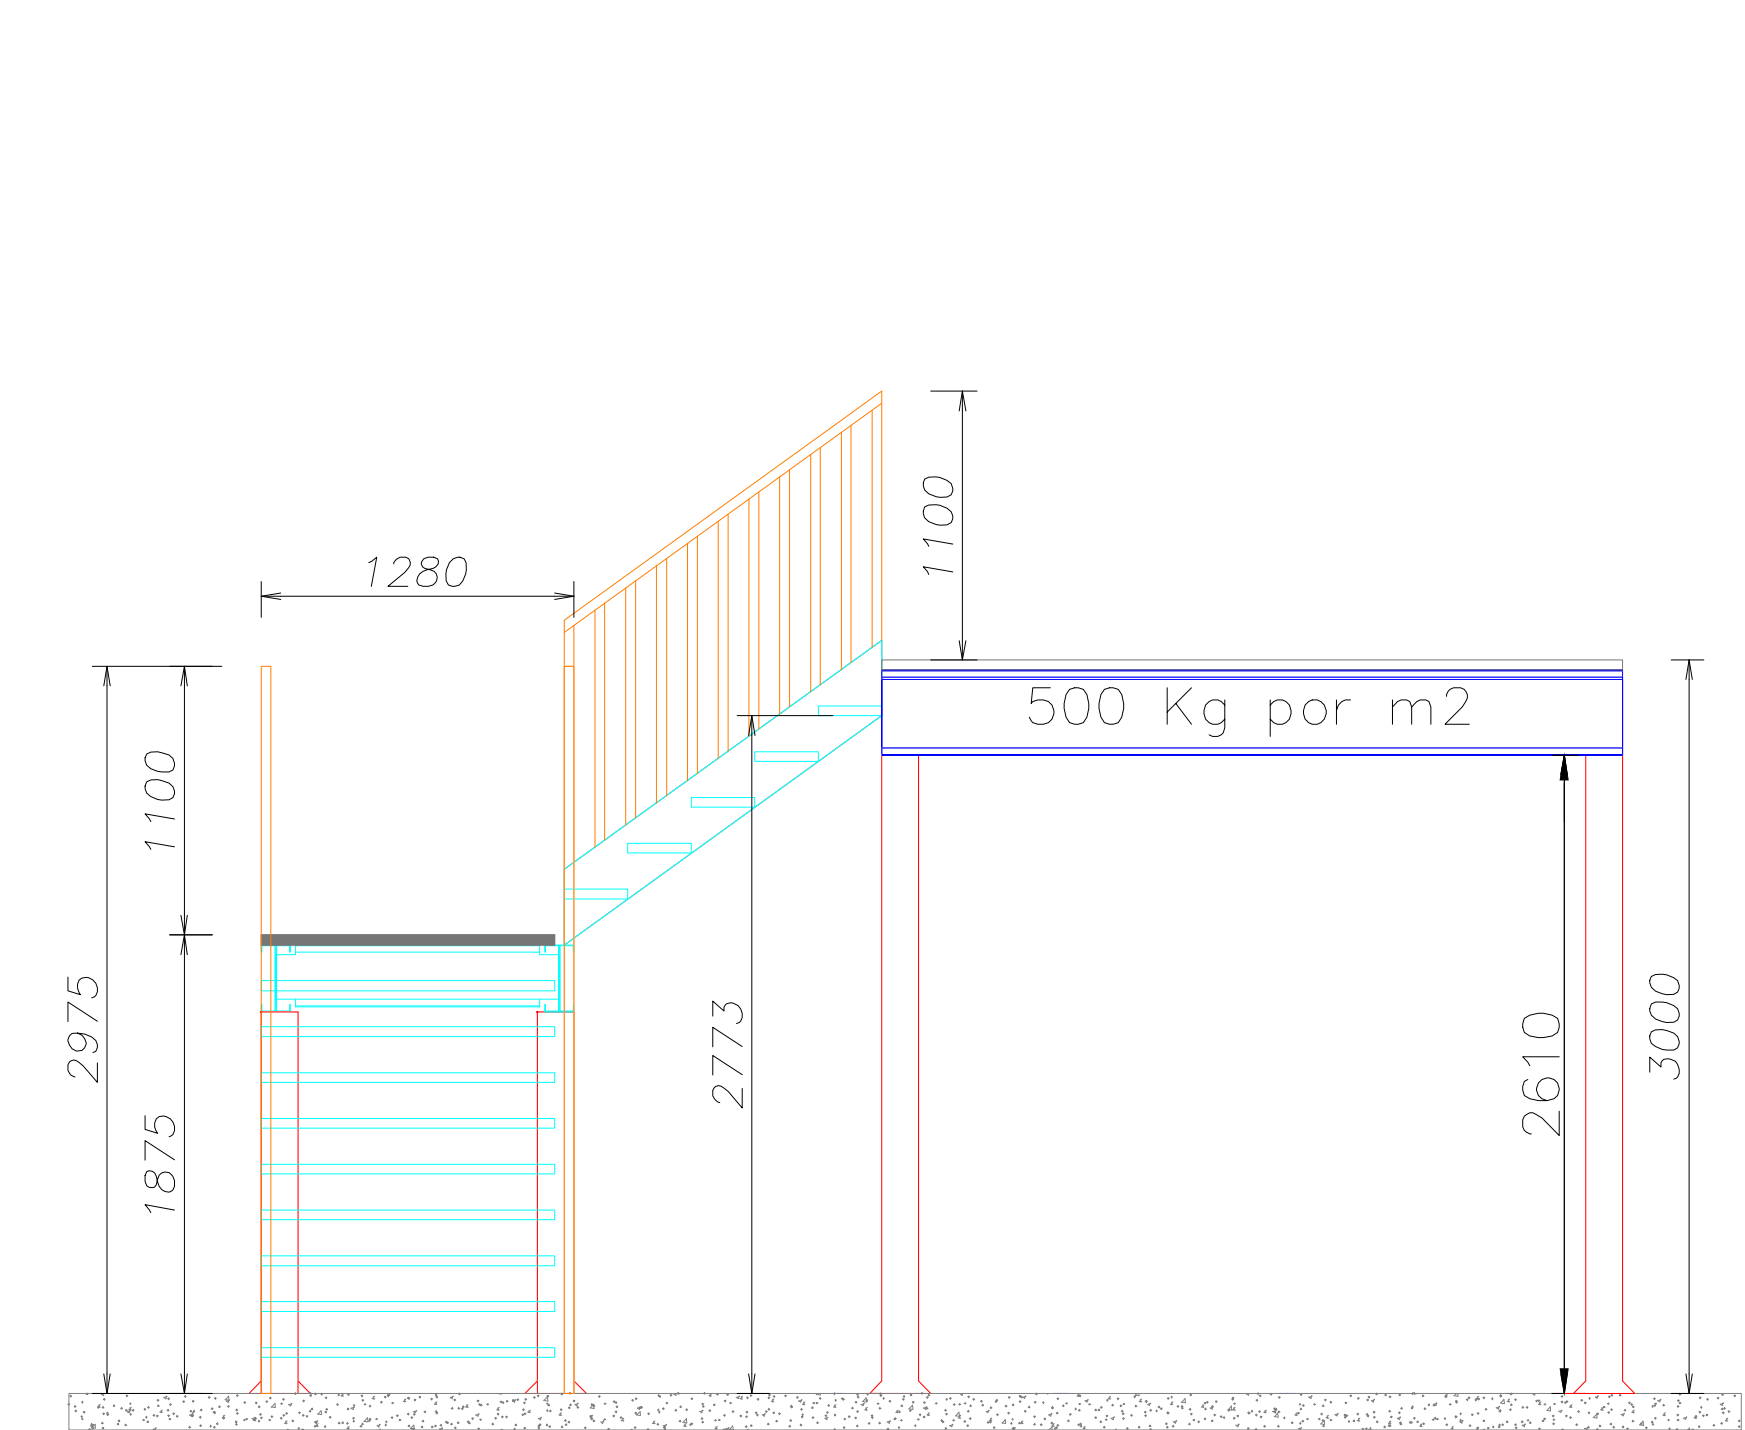


MEZANINO - VISTA LATERAL

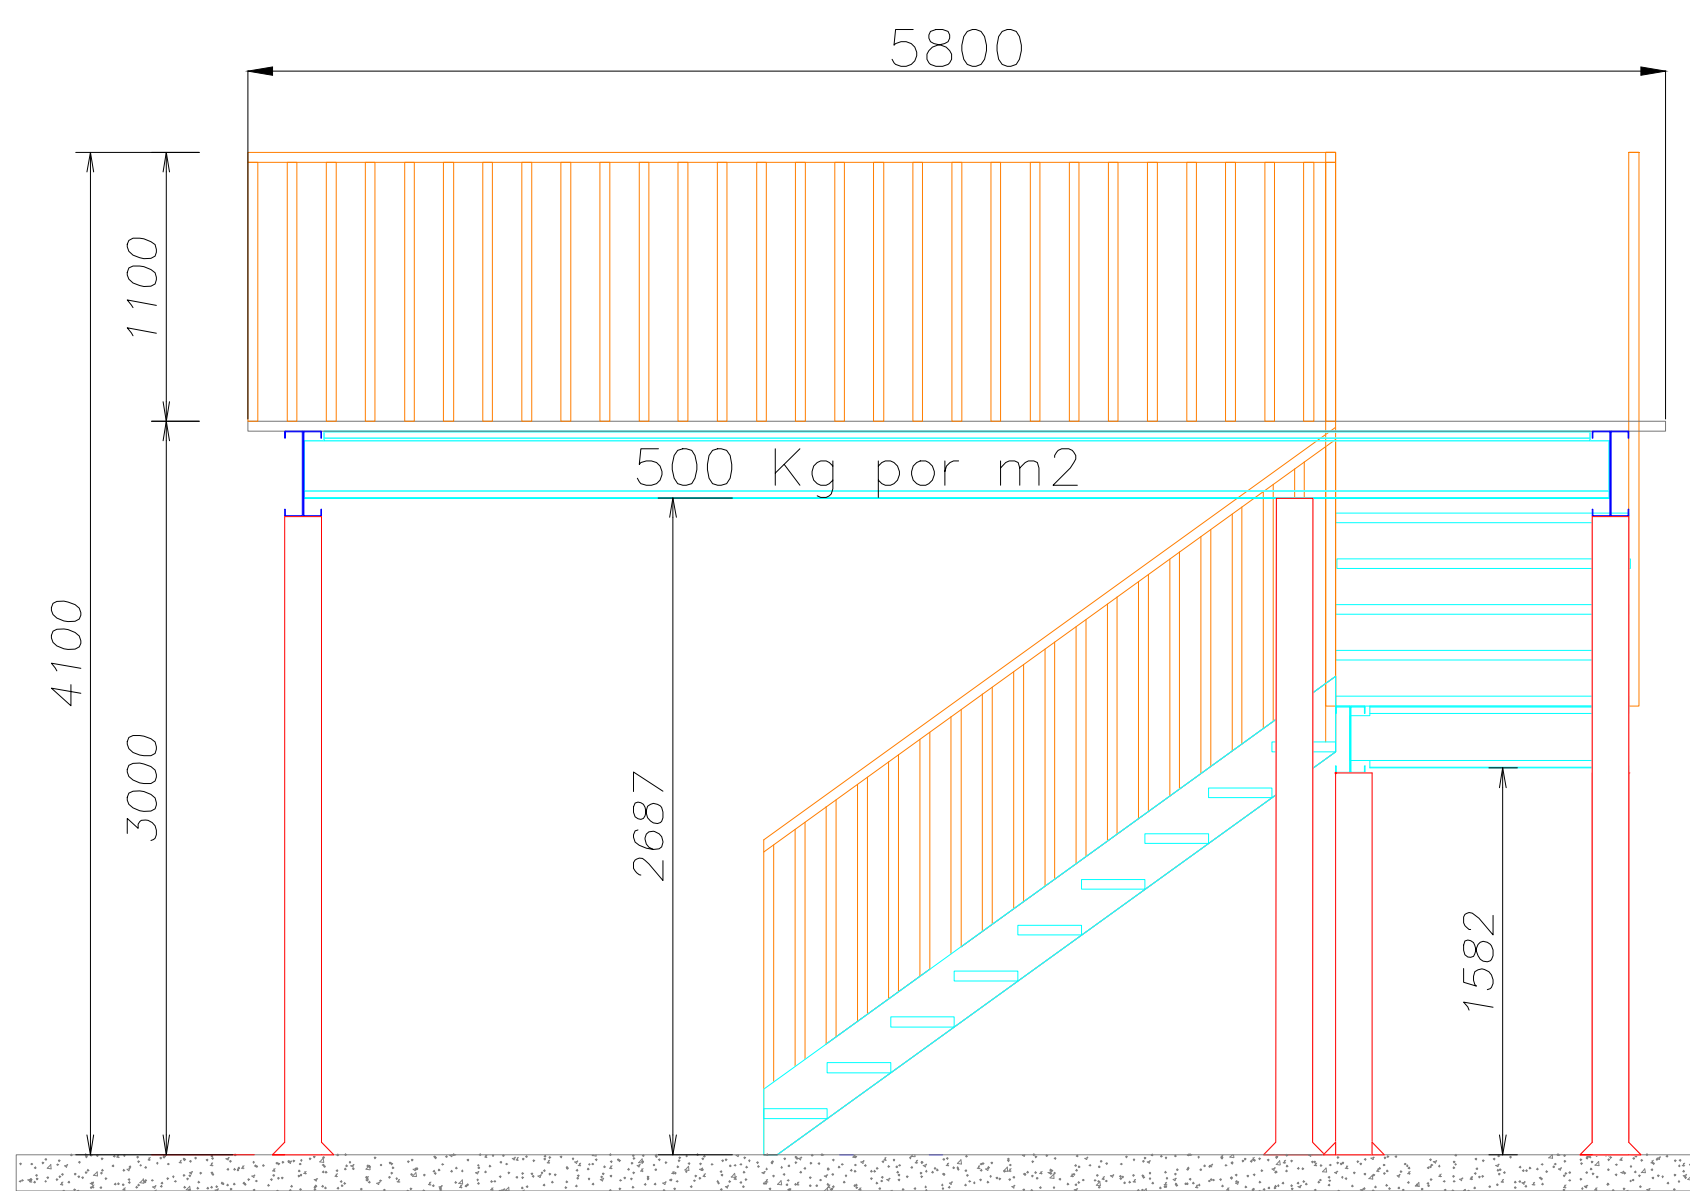


MEZANINO - VISTA FRONTAL

CORTES MEZANINO
Escala: 1:30

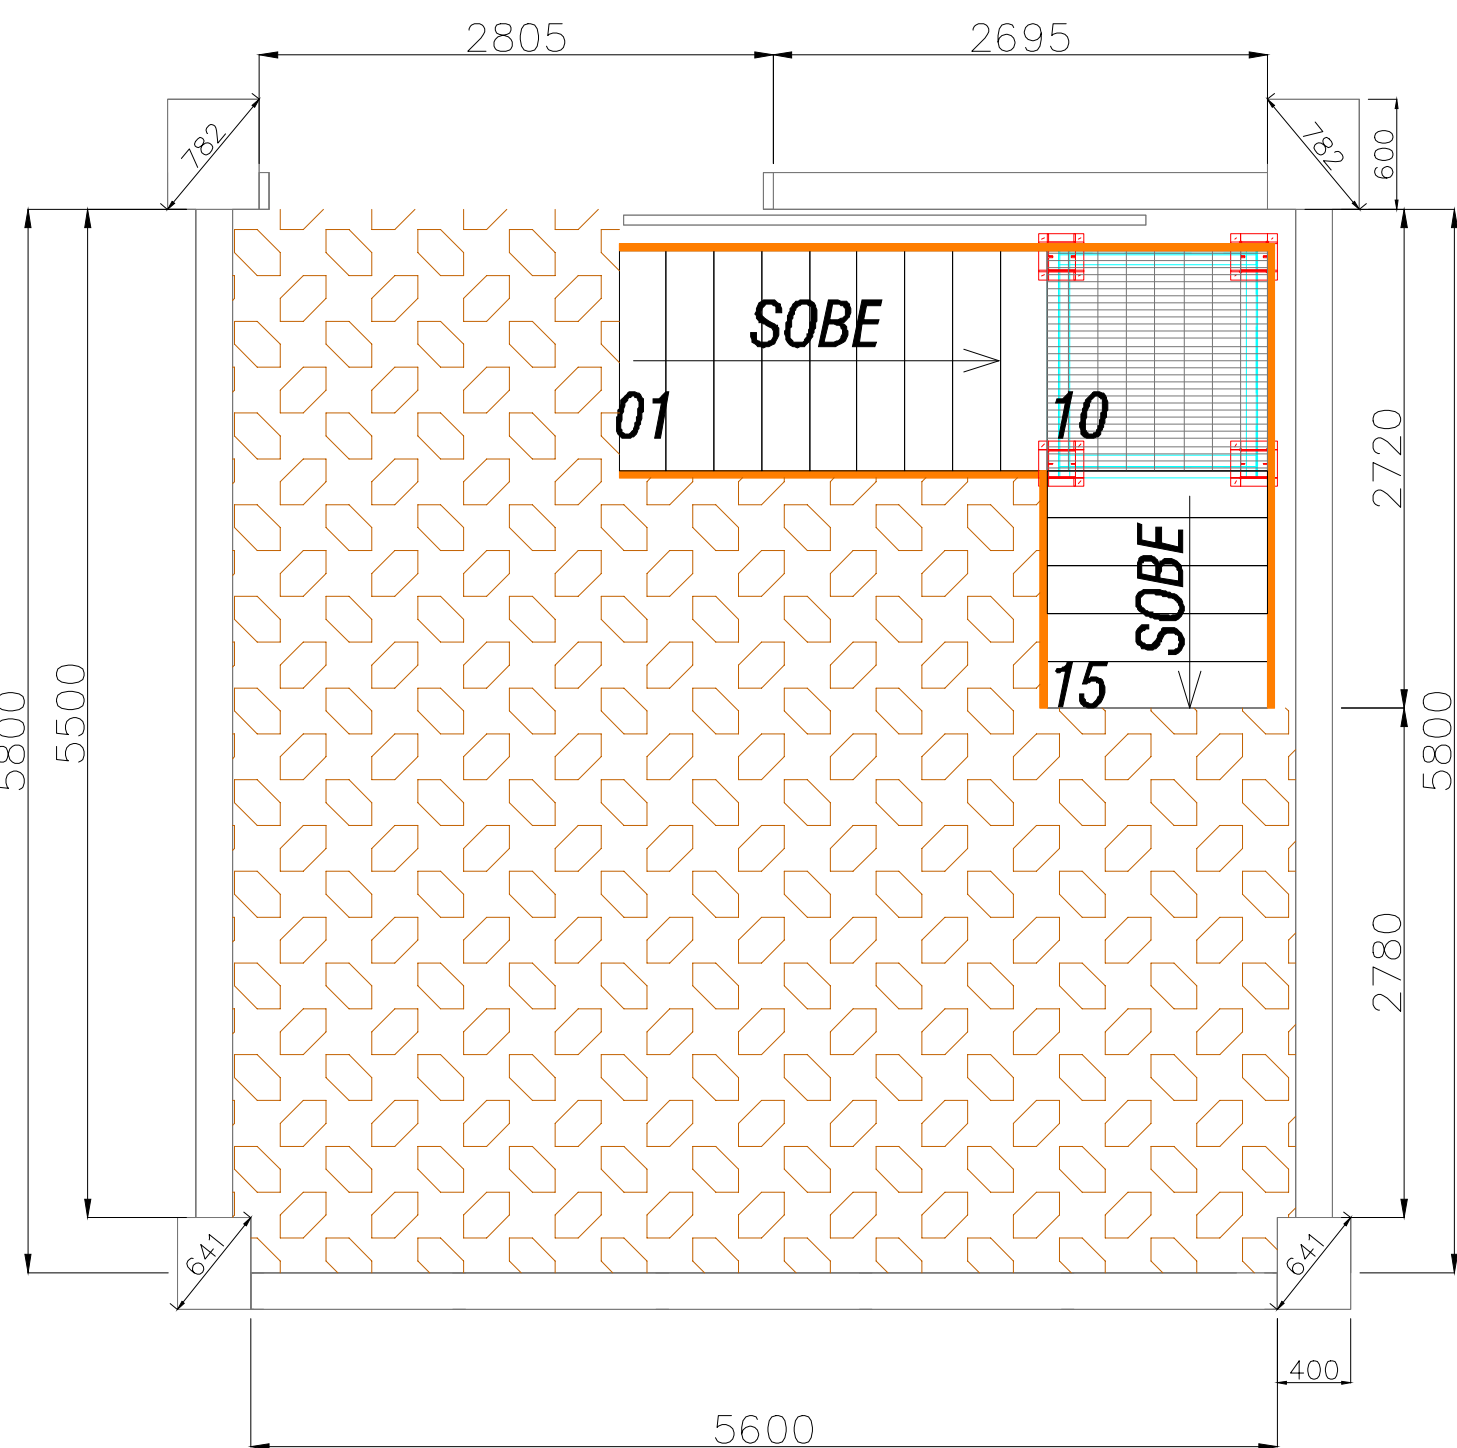

PLANTA BAIXA MEZANINO
Escala: 1:125

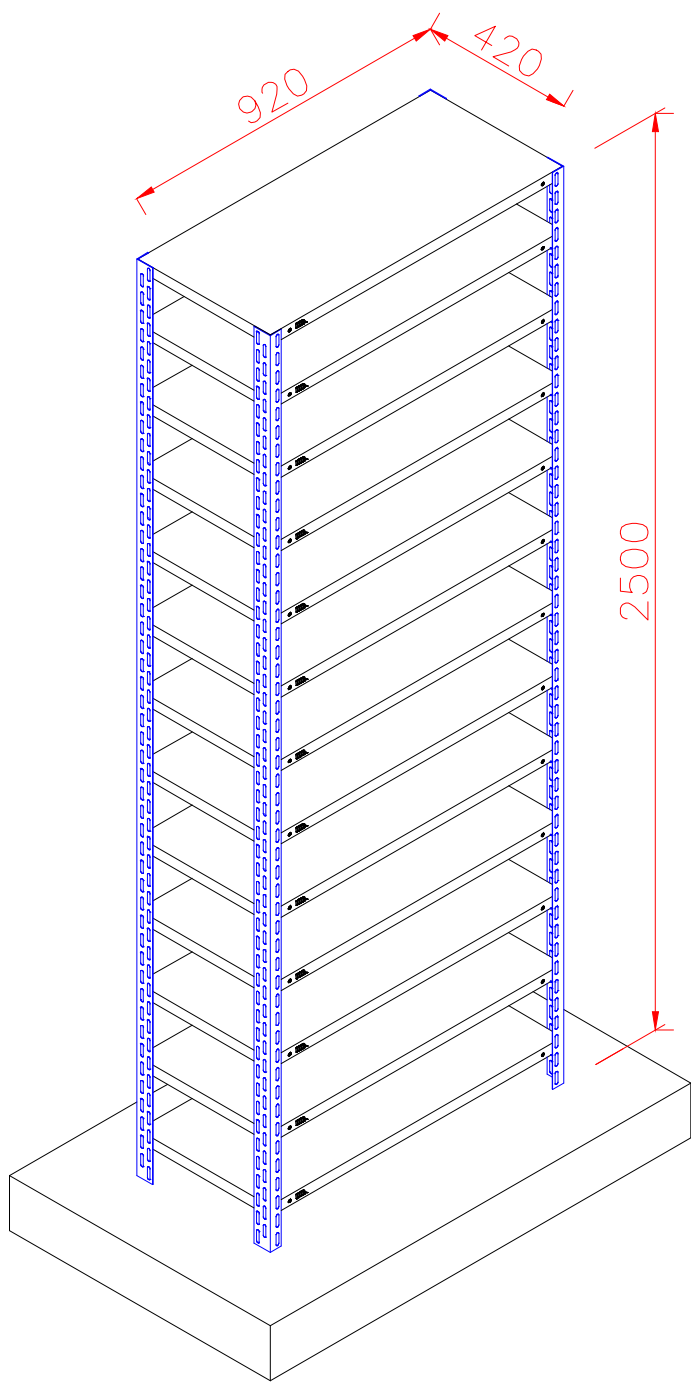

ESTANTE L3 #14 COM 13 NÍVEIS DE BANDEJAS #26 COM PROFUNDIDADE DE 400mm E CAPACIDADE DE CARGA PARA ATÉ 25 Kg.

</



suprainstalações.com.br

Rodovia MO 260 - Km 33 - Areal Rodrigues
Cidade Piraí - RJ - Cep: 30.020-000 - Cidade RJ